

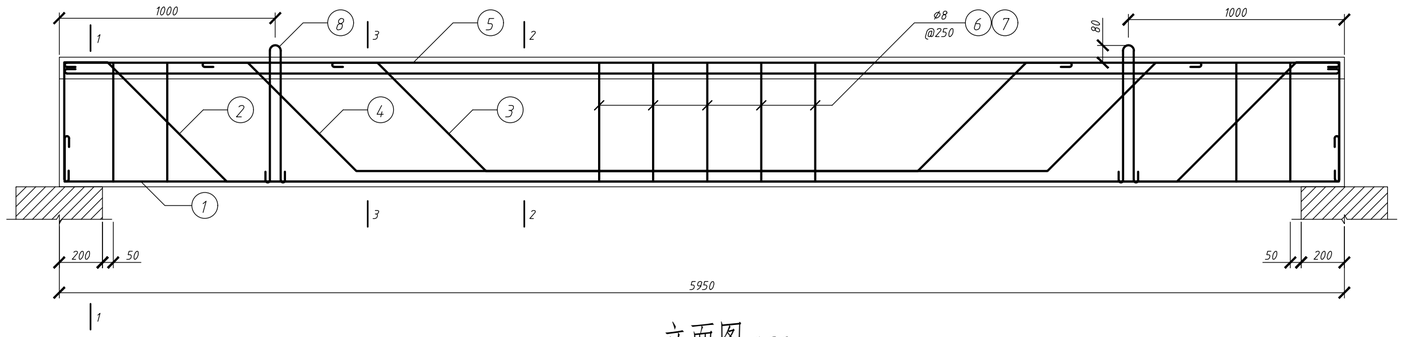



立面图 1:20

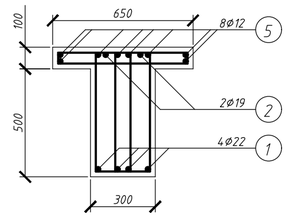


1-1断面图 1:20

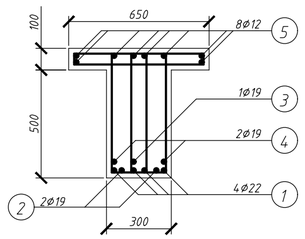

2-2断面图 1:20

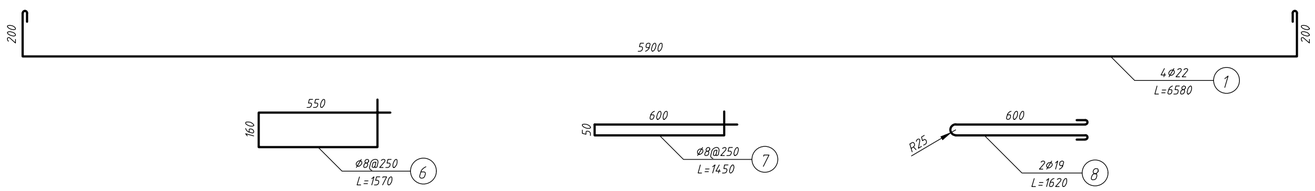

钢筋详图 1:20

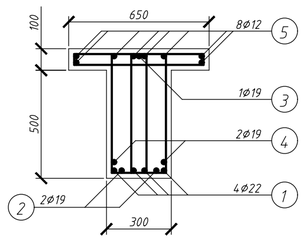

3-3断面图 1:20

钢　筋　表

编号	形状	直径	长度（mm）	根数	全部构件用量			备注
					总根数	总长度（m）	总质量（kg）	
①		22	6580	4	80	526.40	1568.00	
②		19	7700	2	40	308.40	1482.00	
③		19	4060	1	20	81.20	862.00	
④		19	5260	2	40	210.40	4958.00	
⑤		12	6050	8	160	968.00	860.00	
⑥		8	1570	50	1000	1570.00	620.00	
⑦		8	1450	25	500	725.00	286.00	
⑧		19	1620	2	40	64.80	69.00	

说明：

1. 混凝土强度等级为C35
2. 弯起钢筋均弯起45°

钢筋混凝土T 形梁配筋图		比例	1:20
		图号	06
制图	张三	2023.11.9	大连理工大学
审核			建土2307 班